


INTERIOR
RENOVATION
AE NYC DESIGN
CENTER
AMERICAN EAGLE
OUTFITTERS

393-401 Fifth Ave.
New York NY 10016

CONSULTANT

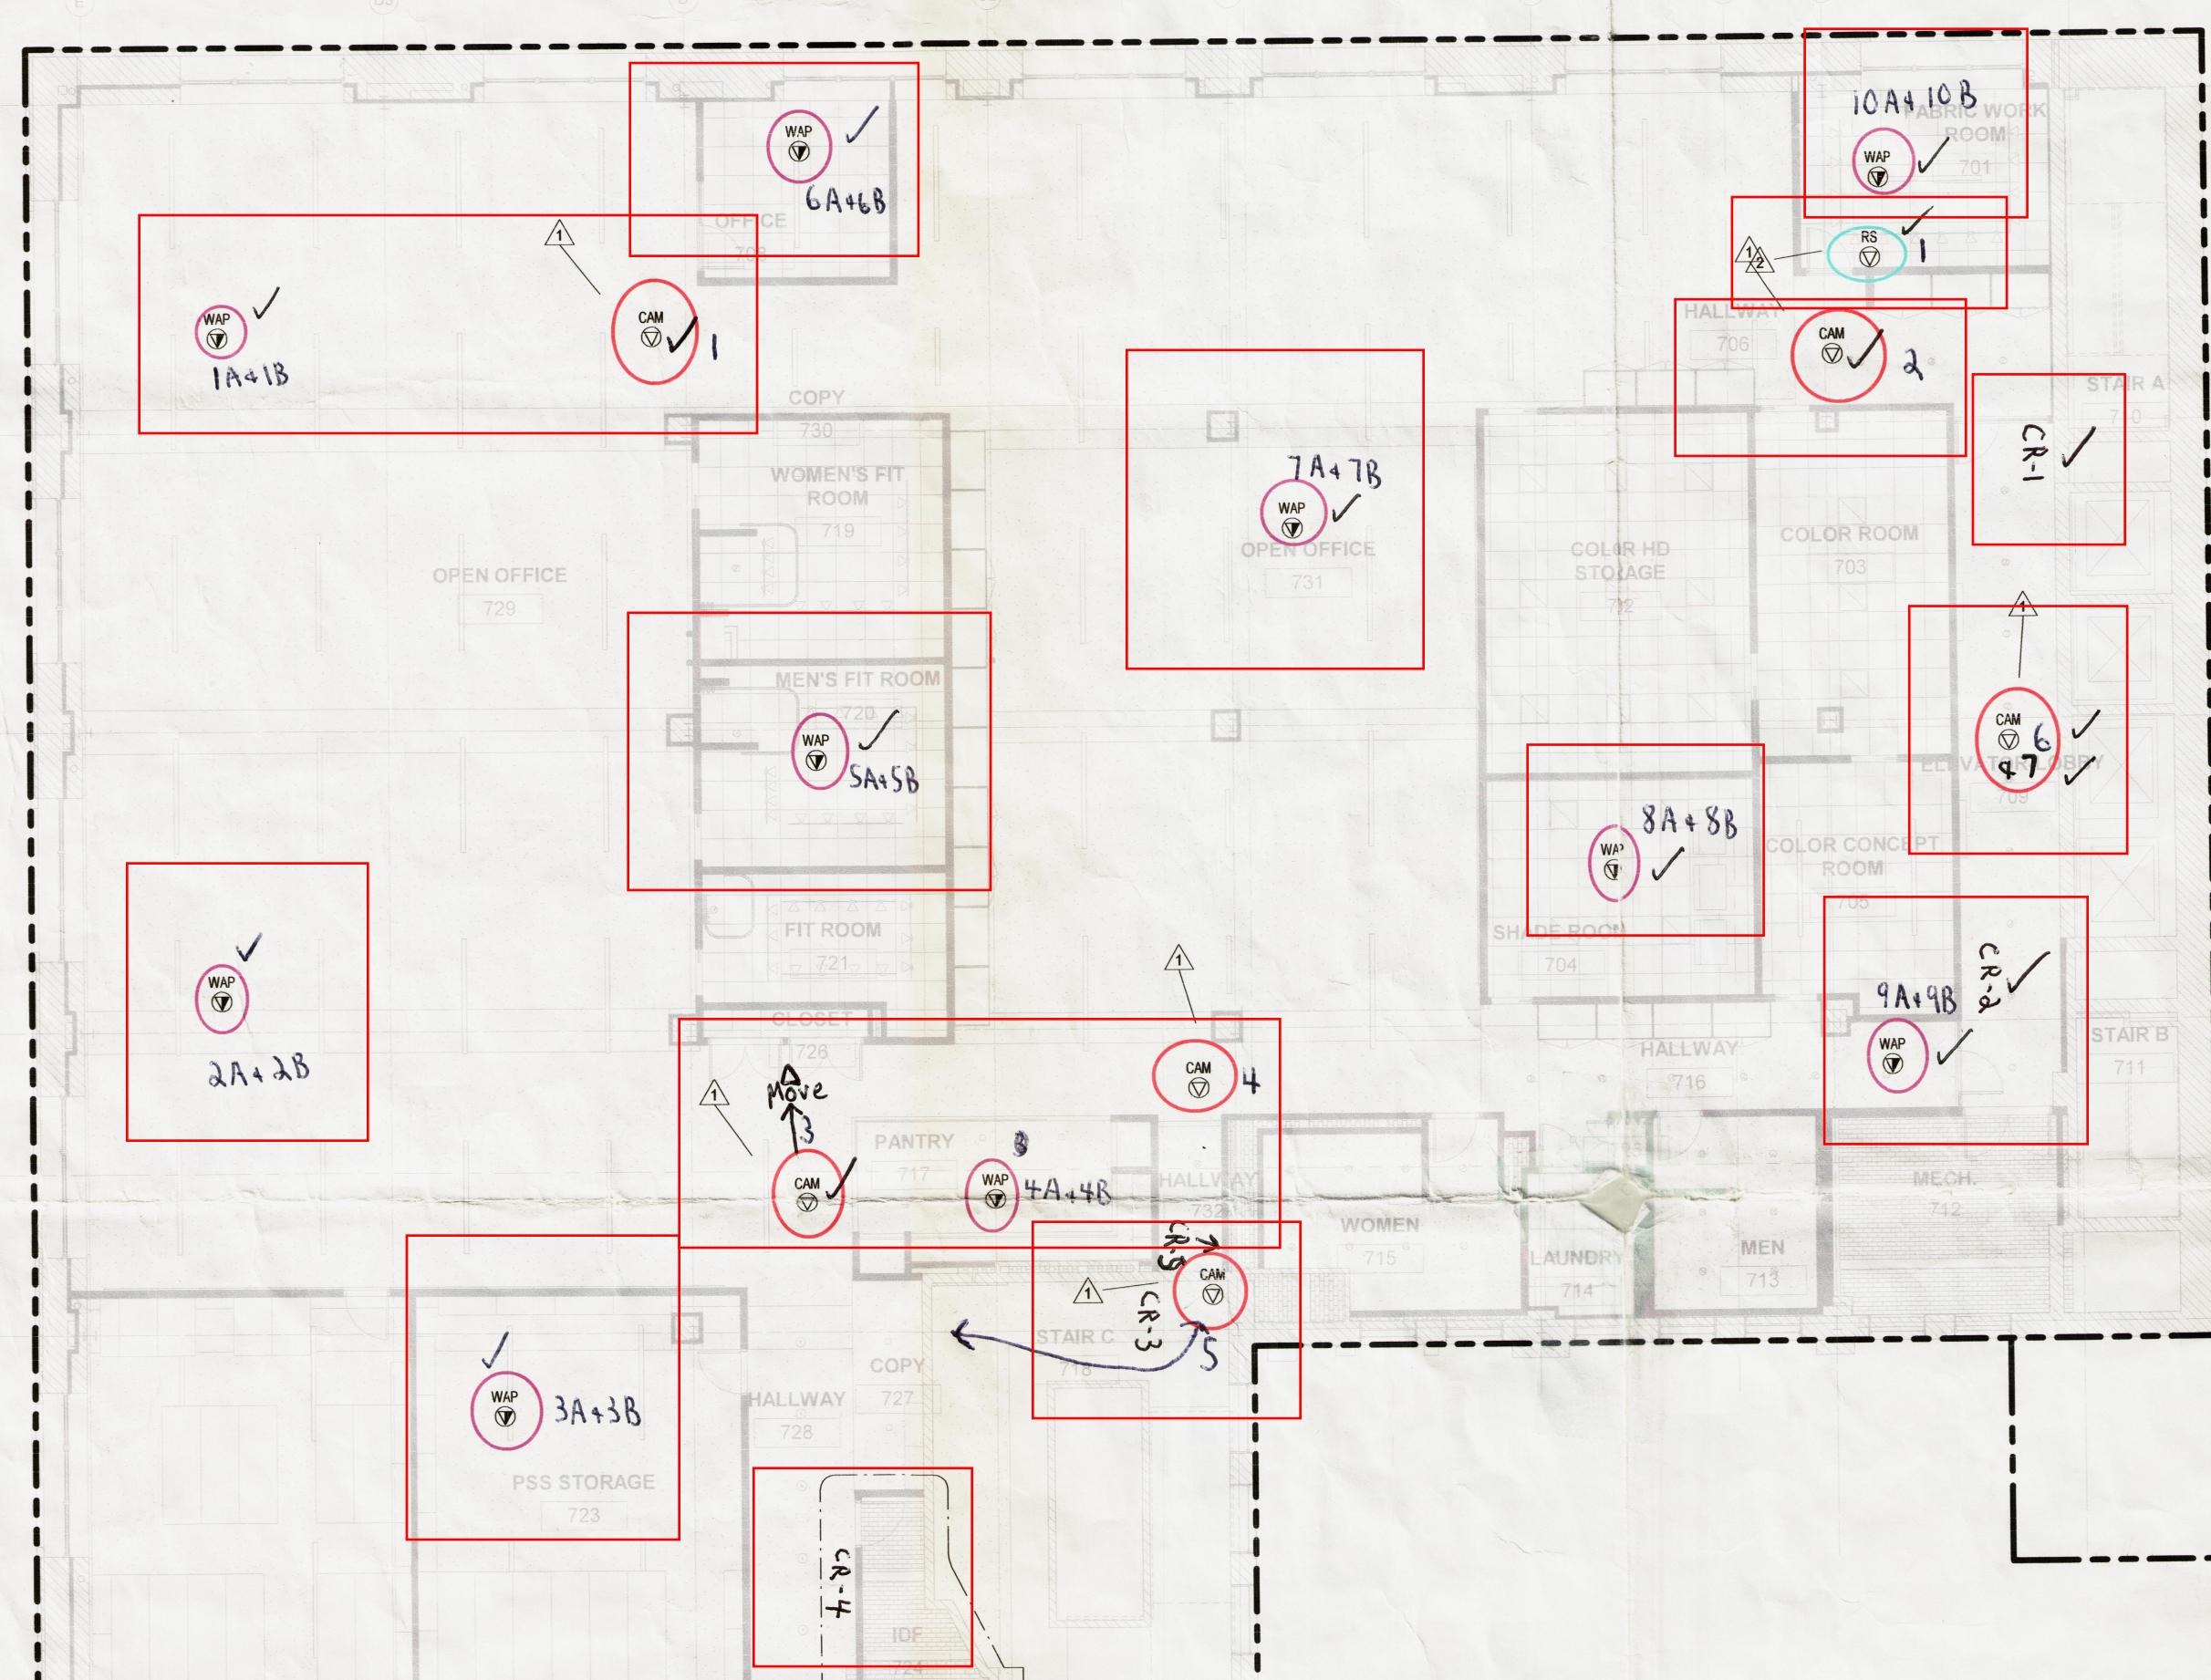

PHASE 2A AREA

- AP 2 Cat 6A 10 locs AP-01 TO 10
- Cam 1 Cat 6A 6 locs CAM-1 TO 6
- RS 1 Cat 6A 1 loc RS-1

AEO 17650
Phase 2 - 7th Floor
401 Fifth Avenue
NY, NY 10016

lga PARTNERS

1425 Forbes Ave. Suite 400 Pittsburgh, PA 15219
P 412.243.3438 F 412.243.4747

These drawings are instruments of the Architect's service
and are the property of LGA Partners. They shall not be
reproduced or used in any way, whatsoever, without the
written permission of LGA Partners. © 2019

DESIGN DEVELOPMENT SET

3	08/27/20	REVISION 3
2	03/06/20	REVISION 2
1	02/26/20	REVISION 1
	10/24/19	90% CD
NO.	DATE	DESCRIPTION

DATE:	09/11/2019
DRAWN BY:	Author
PROJECT NO.:	18433.1
FILE NAME:	18433.1 - AEO NY.rvt

SEVENTH FLOOR TELECOM RCP

TN407

GRAPHIC SCALE:

AP-1	S/N: FCW1916NVAL MAC: 54A274297BFC	AP-10	S/N: FCW1916NVAC MAC: 54A274384F08
AP-2	S/N: FCW1916POHJ MAC: 54A27448A00C	AP-7	S/N: FCW1916NV89 MAC: 788AF4F7A264
AP-4	S/N: FCW1916POJG MAC: 54A2743D0A38	AP-5	S/N: FCW1916POTL MAC: 54A274370689
AP-9	S/N: FCW1916POGV MAC: 54A274489E80	AP-6	S/N: FCW1916POGU MAC: 54A274443A98
AP-8	S/N: FCW1916NV9X MAC: 54A274297C48	AP-3	S/N: FCW1916POH4 MAC: 54A274443A64

17650 - PHSE 2
AEO - 7TH FLOOR
401 FIFTH AVENUE, 7TH FL
NEW YORK, NY 10016

