


INTERIOR  
RENOVATION

**AE NYC DESIGN  
CENTER**

AMERICAN EAGLE  
OUTFITTERS

393-401 Fifth Ave.  
New York NY 10016

CONSULTANT

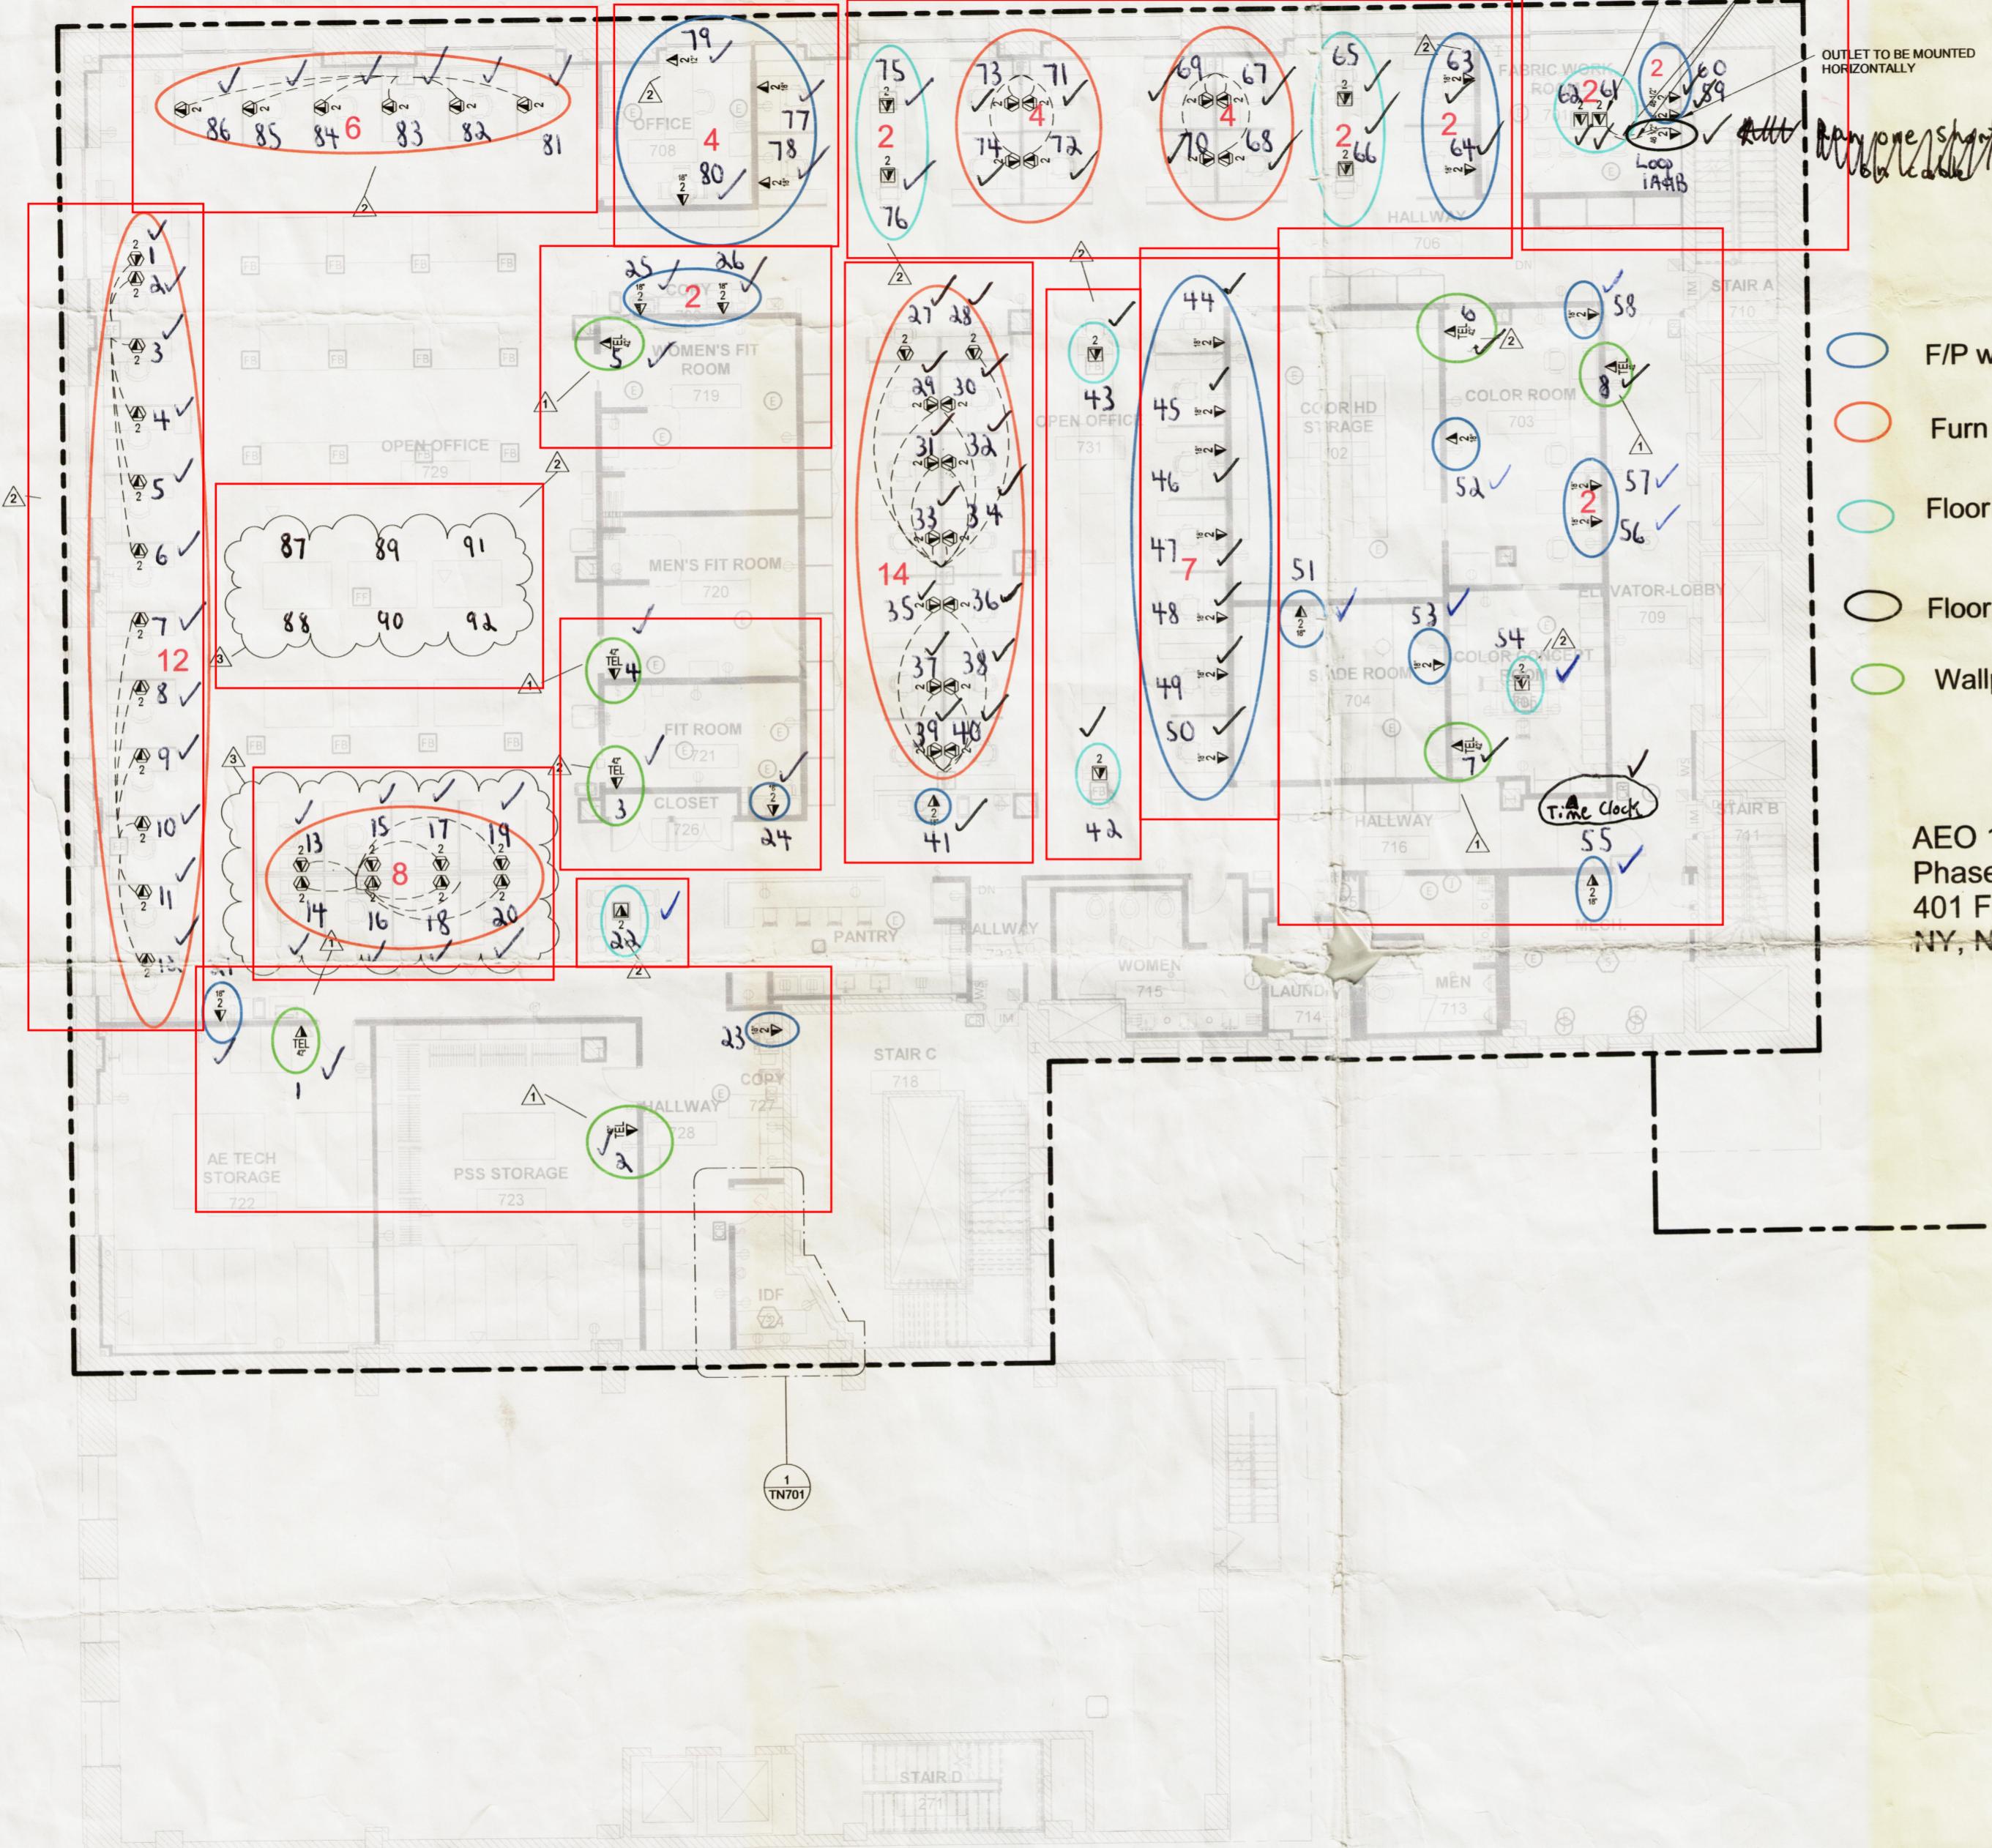

OUTLET SCHEDULE - 7TH FLOOR		
SYMBOL	TYPE	DESCRIPTION
1	2	2-PORT FLOOR BOX MOUNTED DATA OUTLET
1	2	2-PORT FURNITURE MOUNTED DATA OUTLET
1	2	2-PORT WALL MOUNTED DATA OUTLET
CAM		1-PORT ABOVE CEILING SECURITY CAMERA OUTLET
RS		1-PORT ABOVE CEILING ROOM SCHEDULER OUTLET
TEL		1-PORT WALL MOUNTED DATA OUTLET FOR PHONE CONNECTIVITY
WAP		2-PORT ABOVE CEILING WIRELESS ACCESS POINT OUTLET

NOTE: ALL WORKSTATION OUTLETS  
ARE BEING FED THROUGH FF

F/P w/2 Cat 6A cables

Furn w/2 Cat 6A cables

Floor w/2 Cat 6A cables

Floor STP Loop w/2 Cat 6A STP

Wallphone w/1 Cat 6A

28 locs

48 locs

10 locs

1 loc

8 locs

**lga** PARTNERS

1425 Forbes Ave. Suite 400 Pittsburgh, PA 15219

P 412.224.4947

These drawings are instruments of the Architect's service  
and are the property of LGA Partners. They shall not be  
reproduced or used in any way, whatever, without the  
written permission of LGA Partners. © 2019

**DESIGN  
DEVELOPMENT  
SET**

3	08/27/20	REVISION 3
2	03/06/20	REVISION 2
1	02/26/20	REVISION 1
	10/24/19	90% CD
NO.	DATE	DESCRIPTION

DATE: 09/11/2019  
DRAWN BY: Author  
PROJECT NO.: 18433.1  
FILE NAME: 18433.1 - AEO NY.vtf

**SEVENTH FLOOR  
TELECOM PLAN**

**TN207**

GRAPHIC SCALE:

1 7TH FLOOR TELECOM PLAN

TN207

SCALE: 1/8" = 1'-0"



30 to 31  
31 to 29  
32 to 30