


INTERIOR
RENOVATION

**AE NYC DESIGN
CENTER**

AMERICAN EAGLE
OUTFITTERS

393-401 Fifth Ave.
New York NY 10016

CONSULTANT

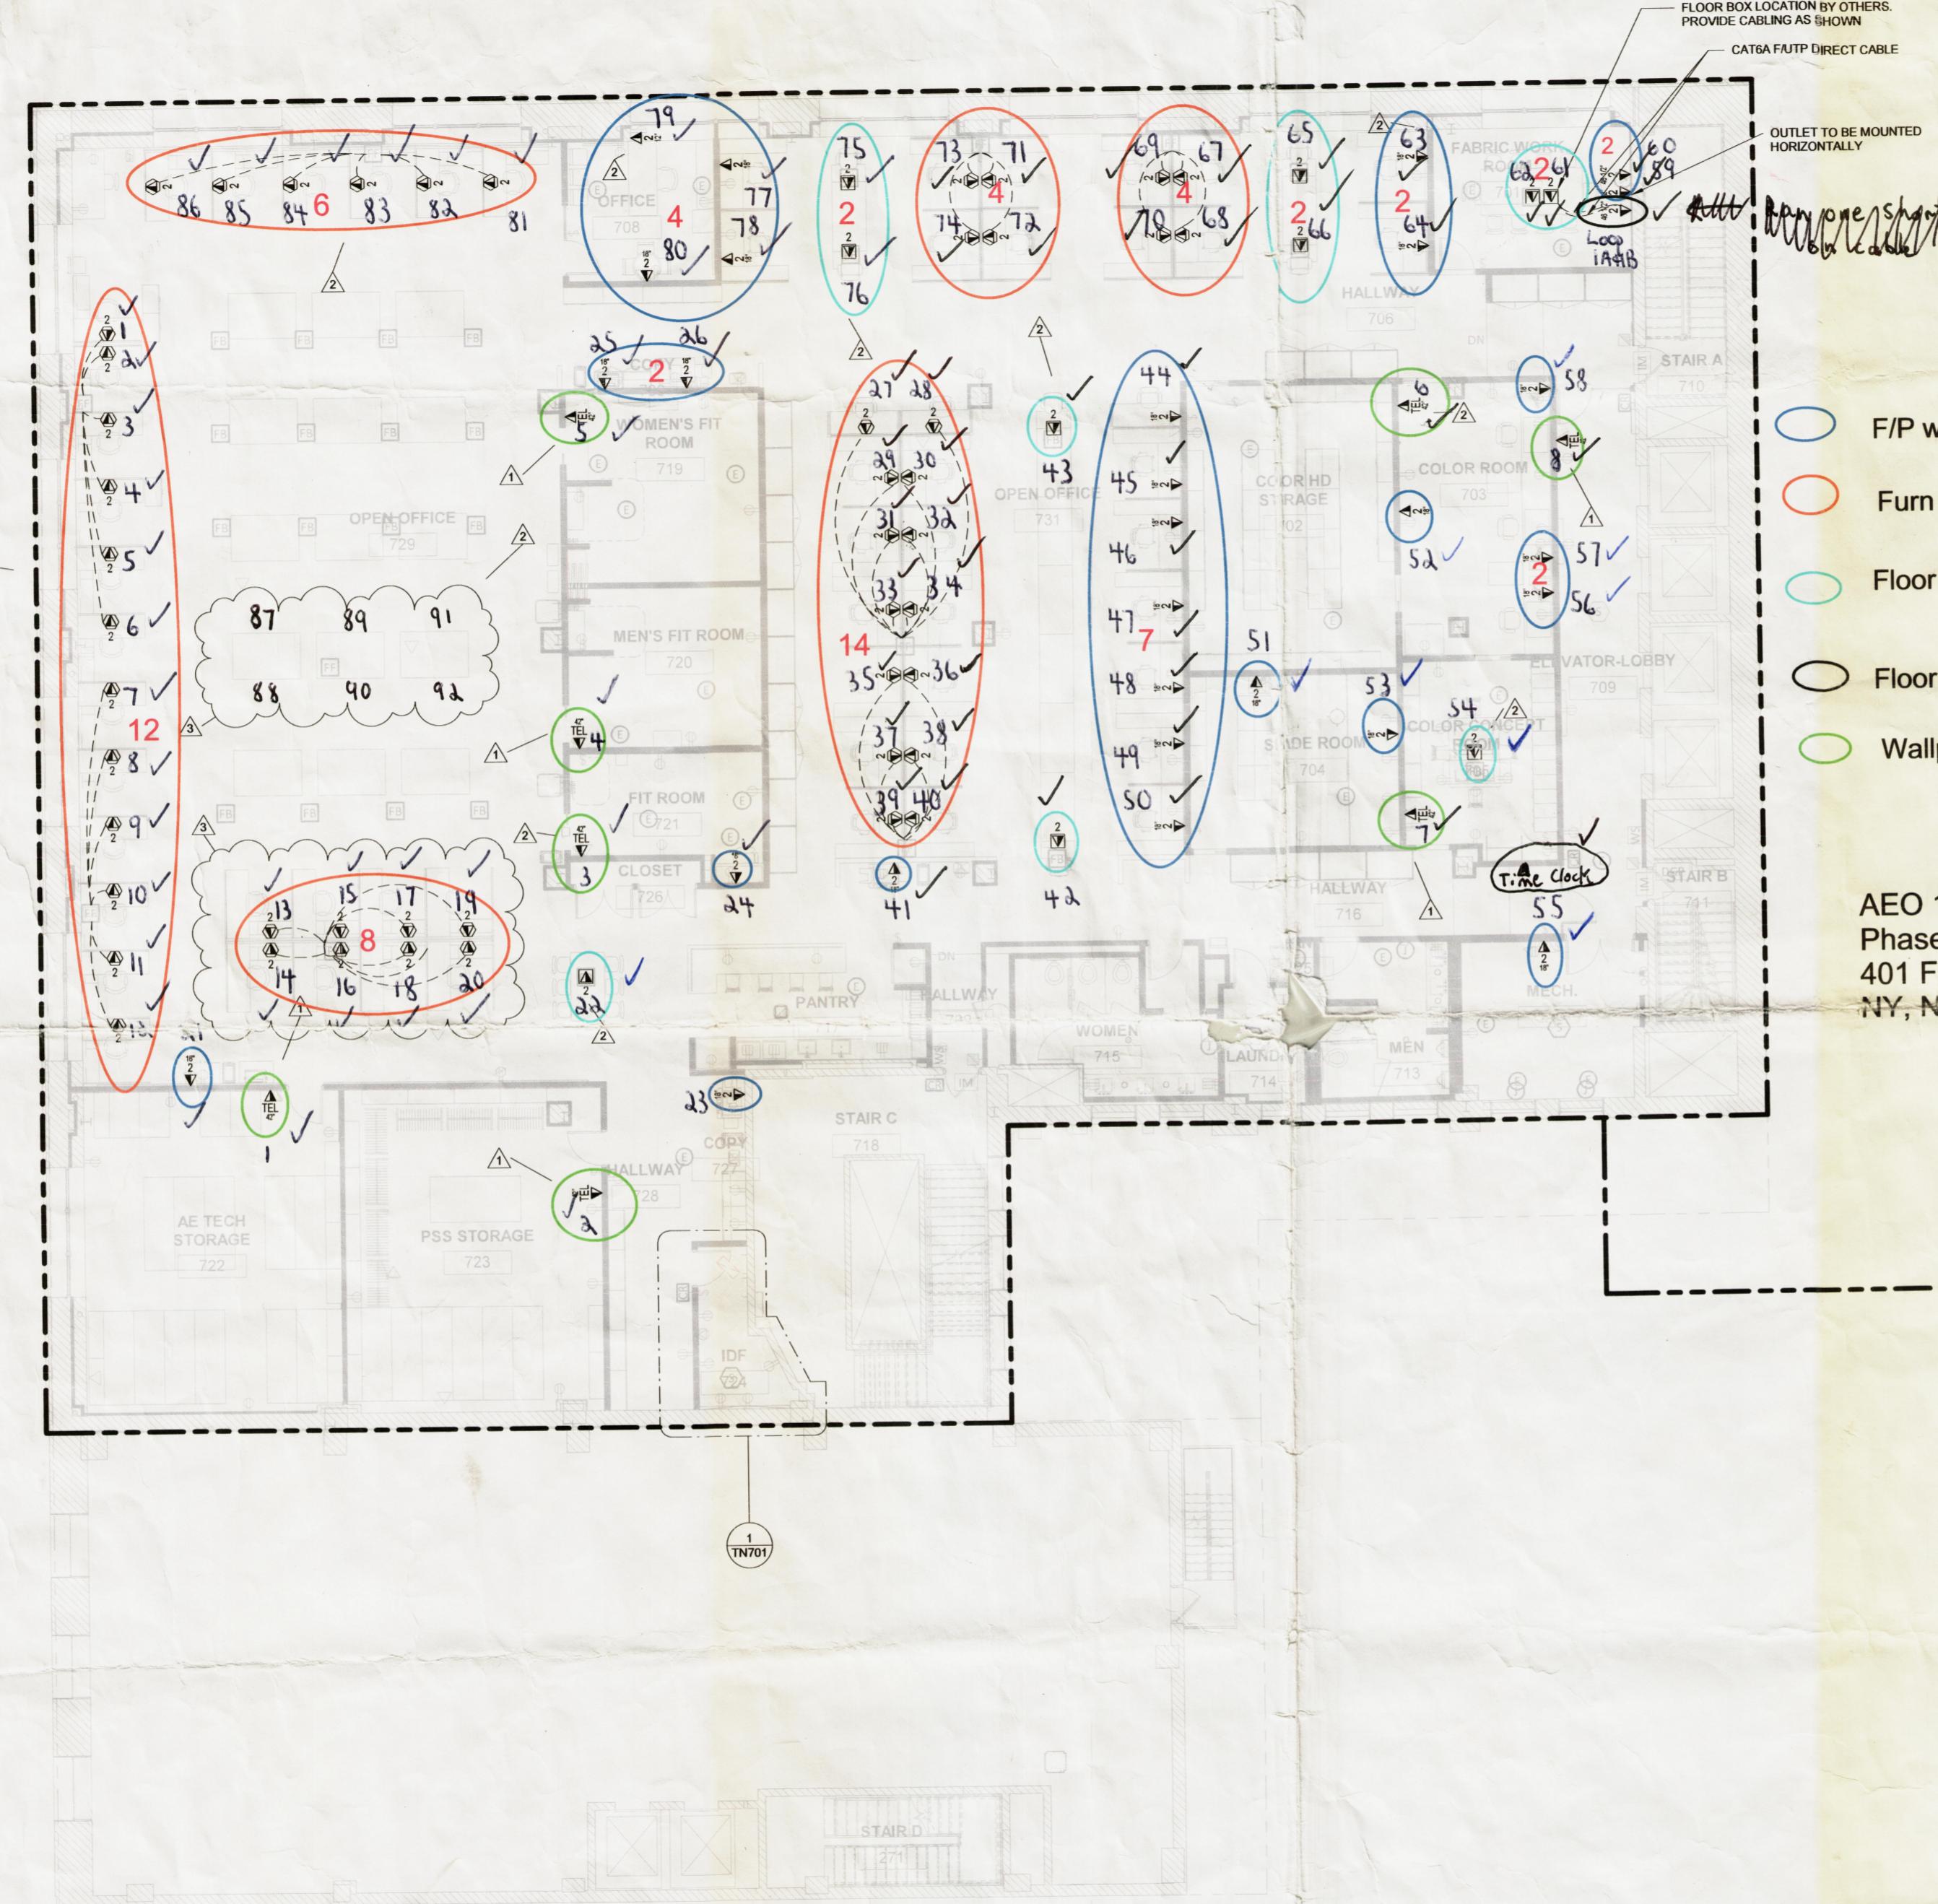

OUTLET SCHEDULE - 7TH FLOOR		
SYMBOL	TYPE	DESCRIPTION
1	2	2-PORT FLOOR BOX MOUNTED DATA OUTLET
1	2	2-PORT FURNITURE MOUNTED DATA OUTLET
1	2	2-PORT WALL MOUNTED DATA OUTLET
CAM		1-PORT ABOVE CEILING SECURITY CAMERA OUTLET
RS		1-PORT ABOVE CEILING ROOM SCHEDULER OUTLET
TEL		1-PORT WALL MOUNTED DATA OUTLET FOR PHONE CONNECTIVITY
WAP		2-PORT ABOVE CEILING WIRELESS ACCESS POINT OUTLET

NOTE: ALL WORKSTATION OUTLETS
ARE BEING FED THROUGH FF

F/P w/2 Cat 6A cables

28 locs

Furn w/2 Cat 6A cables

48 locs

Floor w/2 Cat 6A cables

10 locs

Floor STP Loop w/2 Cat 6A STP

1 loc

Wallphone w/1 Cat 6A

8 locs

#1 to 92

LOOP-1

WP-1 to 8

AEO 17650
Phase 2 - 7th Floor
401 Fifth Avenue
NY, NY 10016

lga PARTNERS

1425 Forbes Ave. Suite 400 Pittsburgh, PA 15219

P 412.224.4947

These drawings are instruments of the Architect's service
and are the property of LGA Partners. They shall not be
reproduced or used in any way, whatever, without the
written permission of LGA Partners. © 2019

**DESIGN
DEVELOPMENT
SET**

3	08/27/20	REVISION 3
2	03/06/20	REVISION 2
1	02/26/20	REVISION 1
	10/24/19	90% CD
NO.	DATE	DESCRIPTION

DATE: 09/11/2019
DRAWN BY: Author
PROJECT NO.: 18433.1
FILE NAME: 18433.1 - AEO NY.vtf

**SEVENTH FLOOR
TELECOM PLAN**

TN207

GRAPHIC SCALE:

1 7TH FLOOR TELECOM PLAN
TN207
SCALE: 1/8" = 1'-0"

31 to 29
32 to 30
30 to 31
31 to 32

